



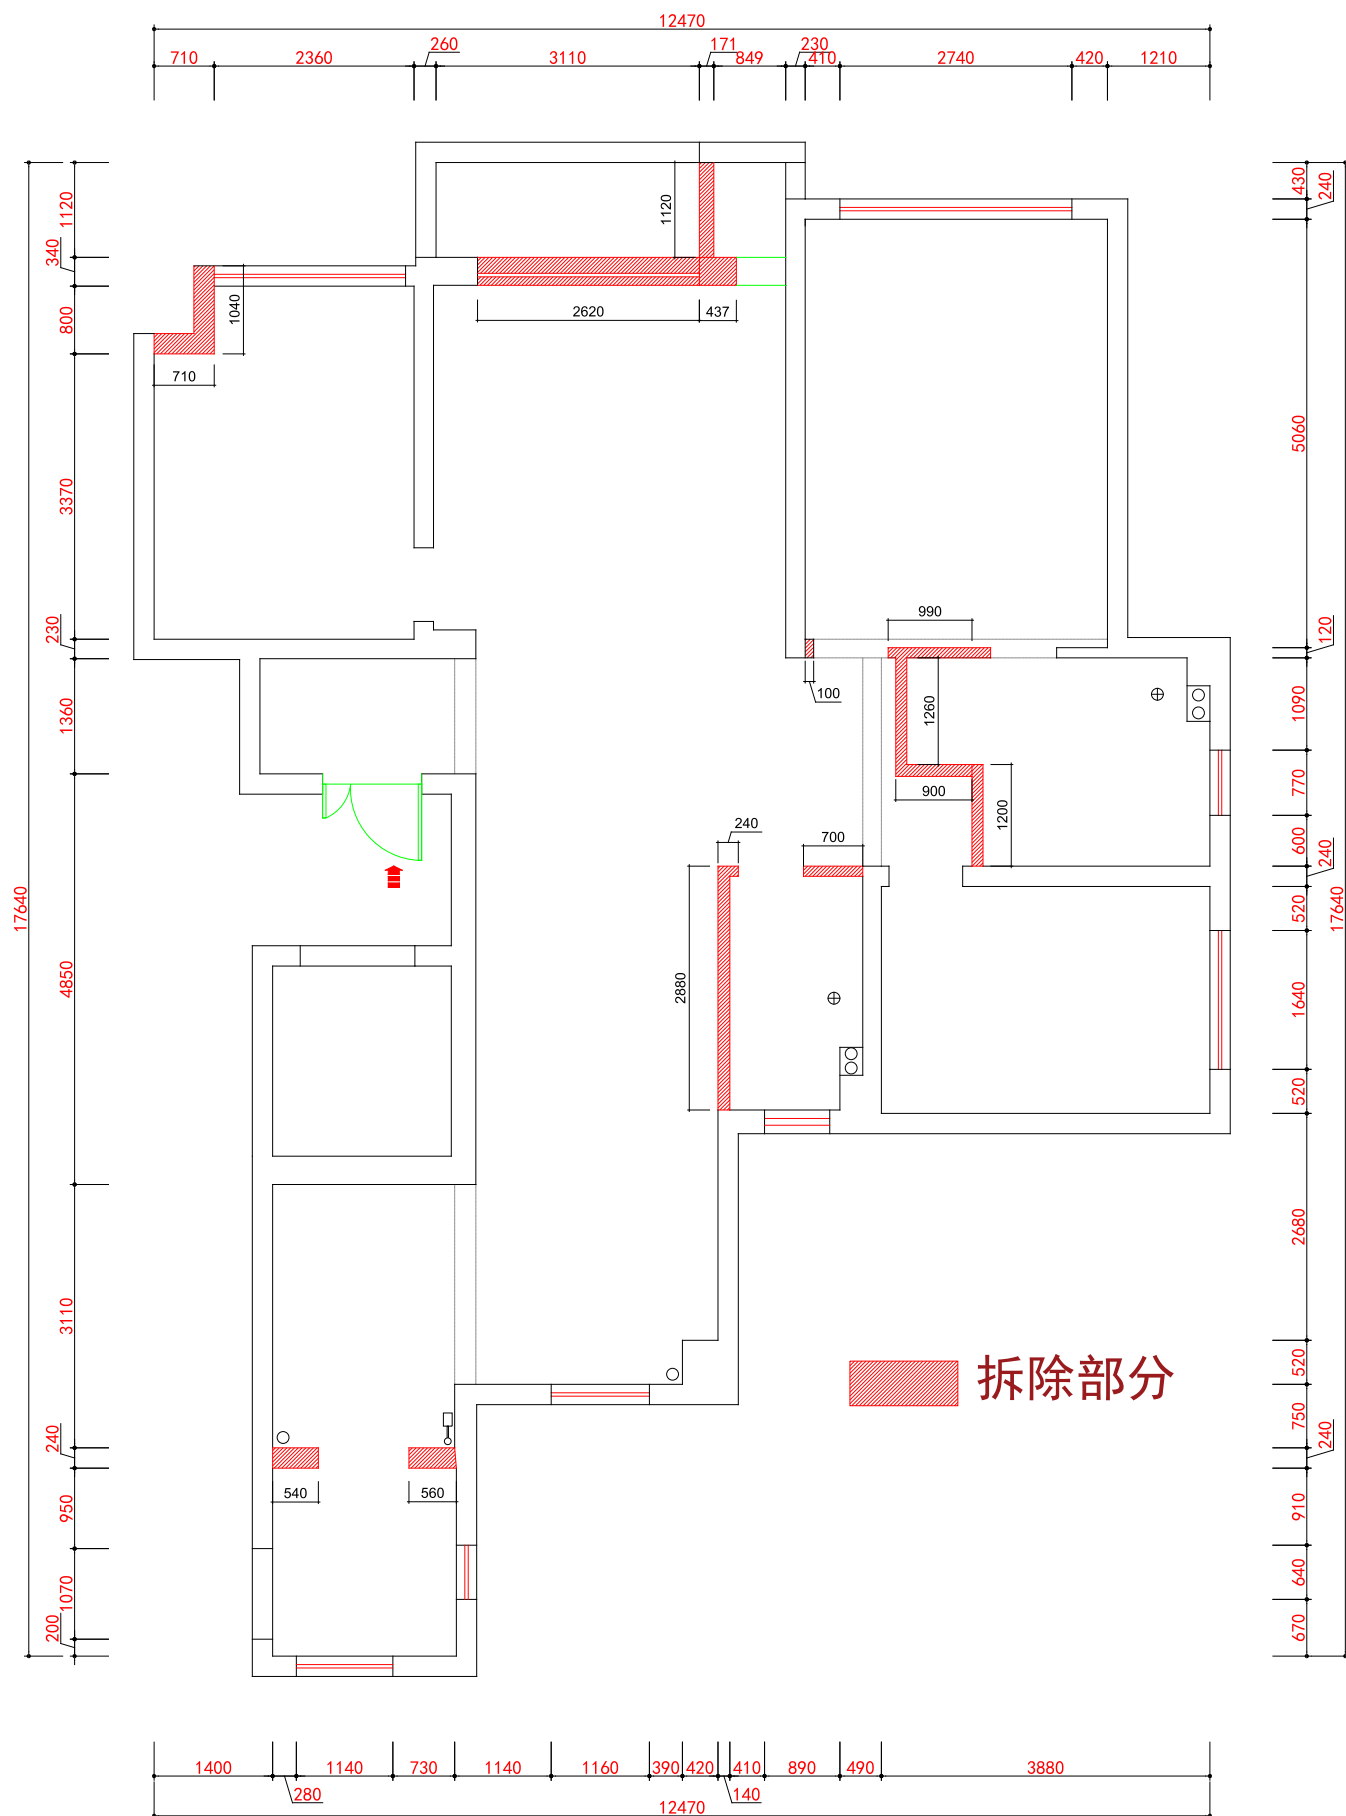


拆除图

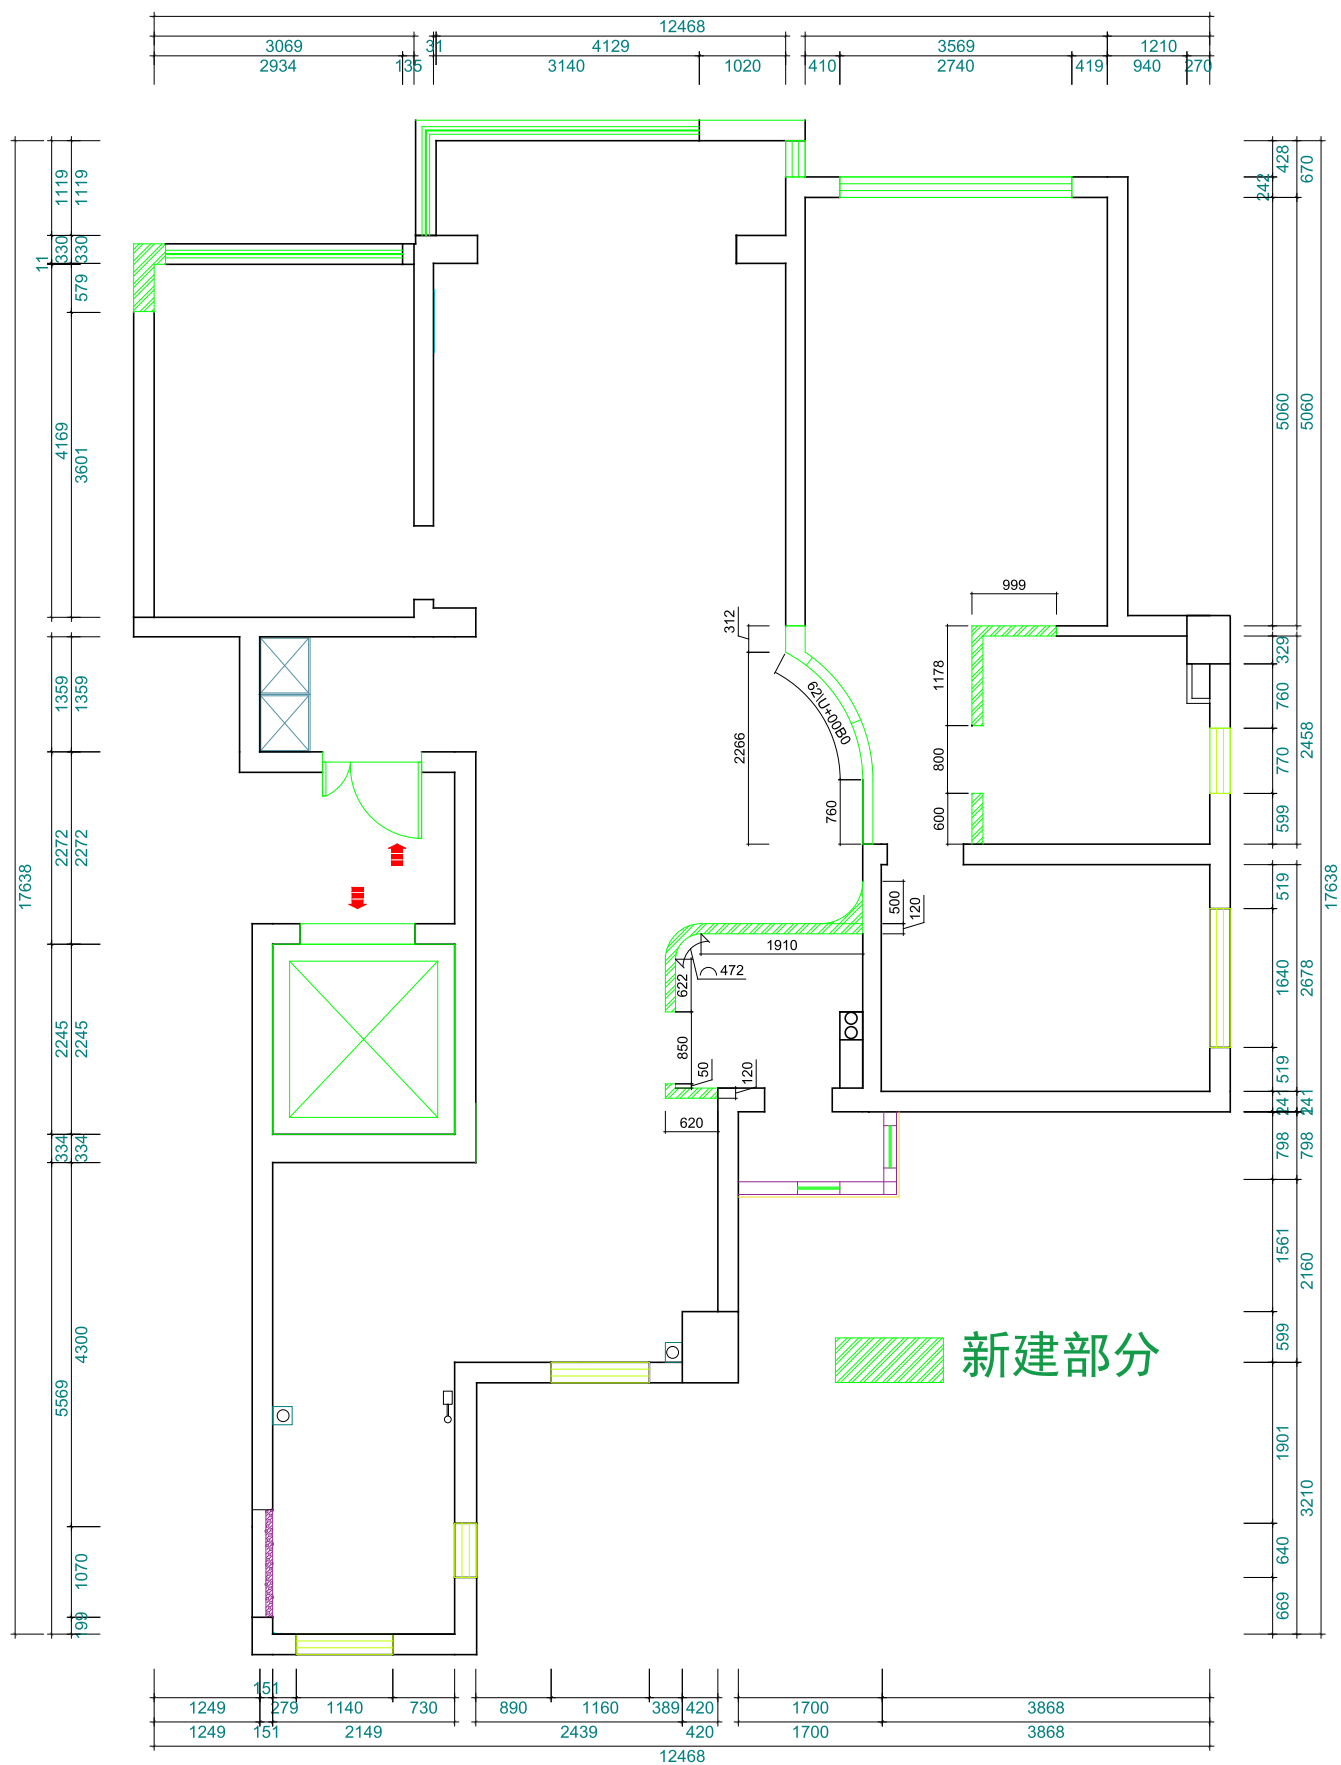


砌筑图




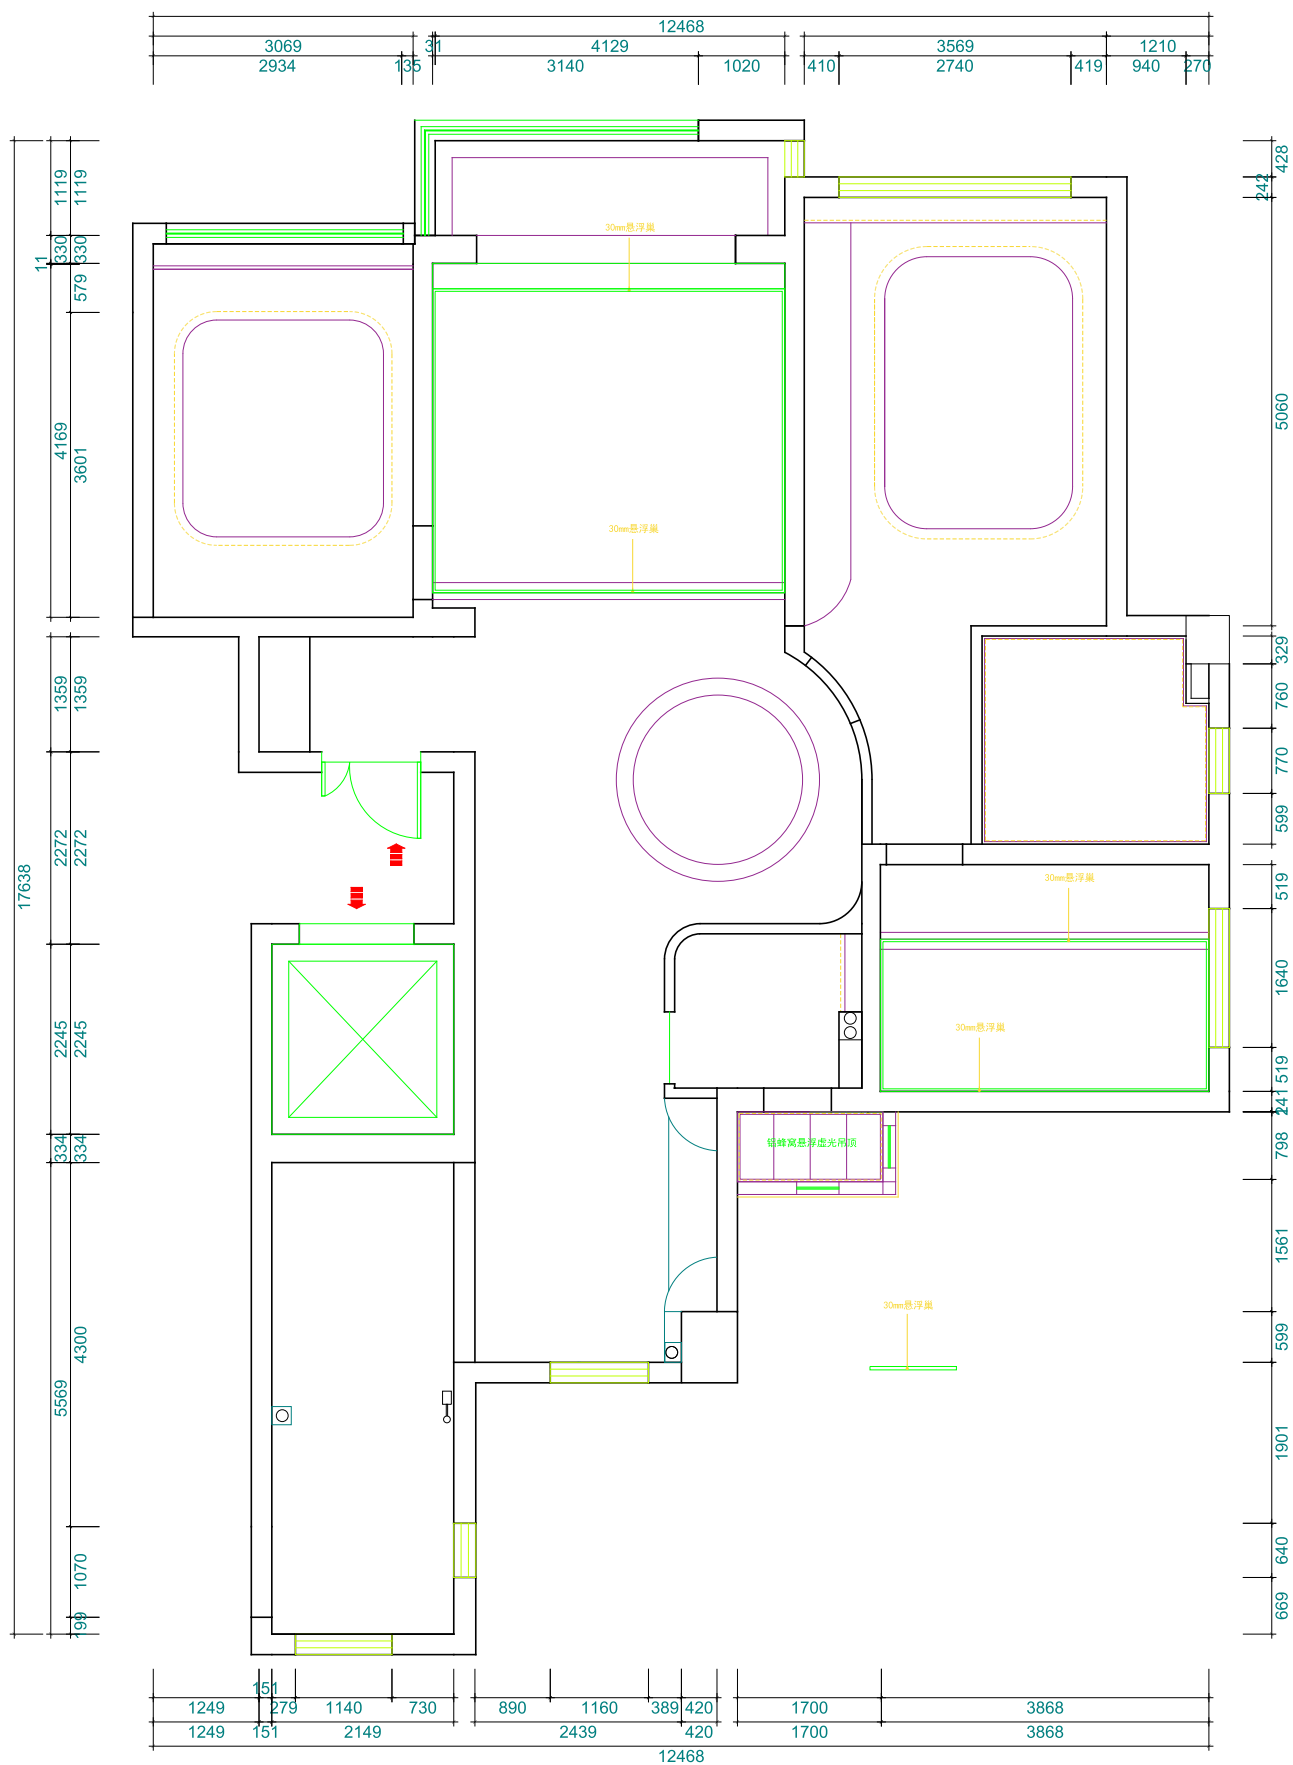

悬浮铝型材位置图

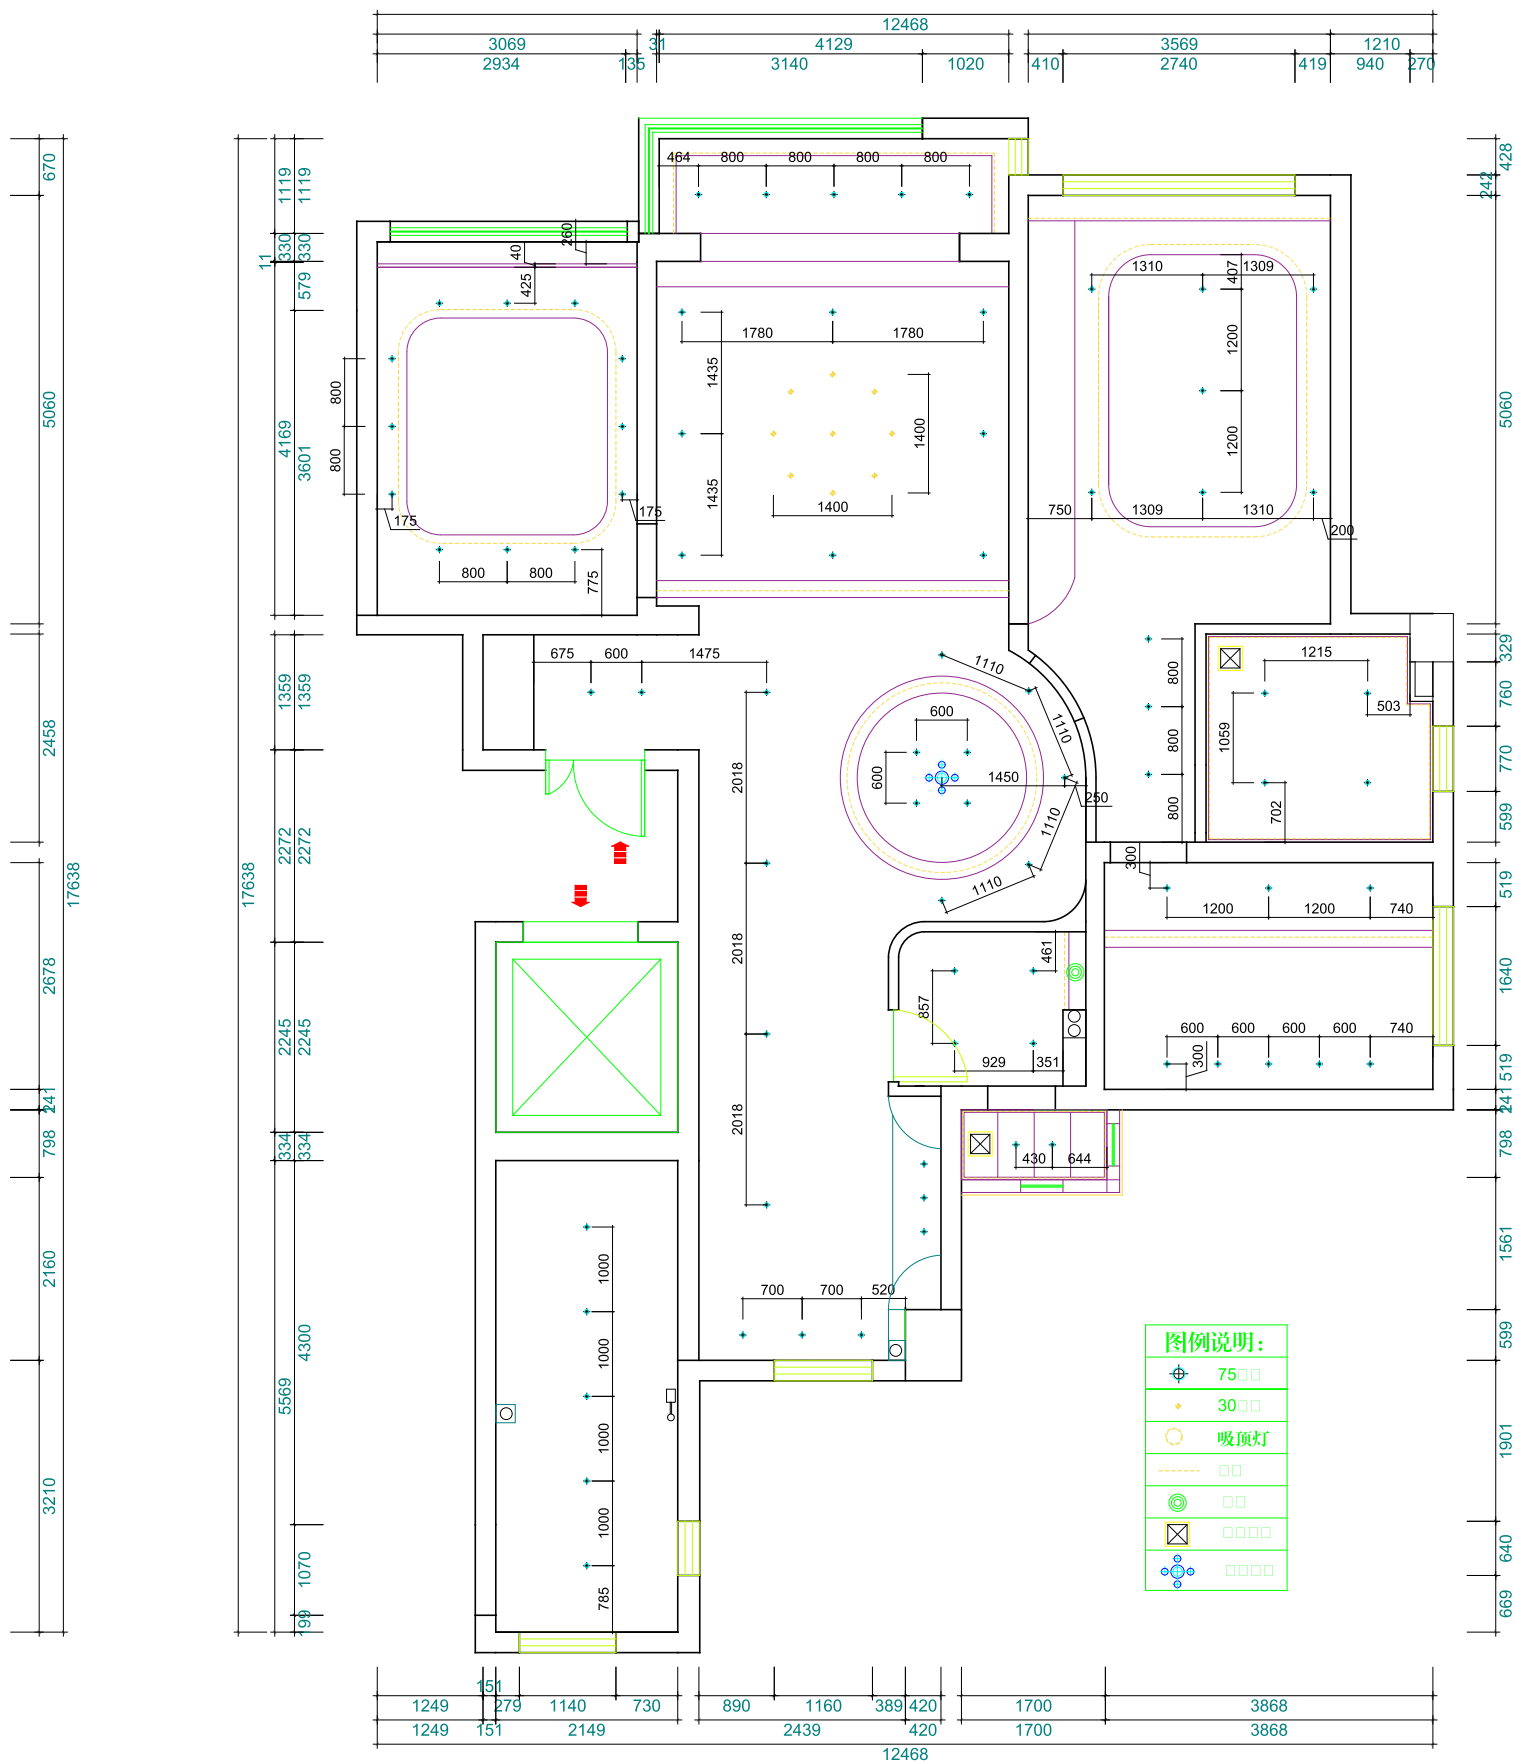


灯位图

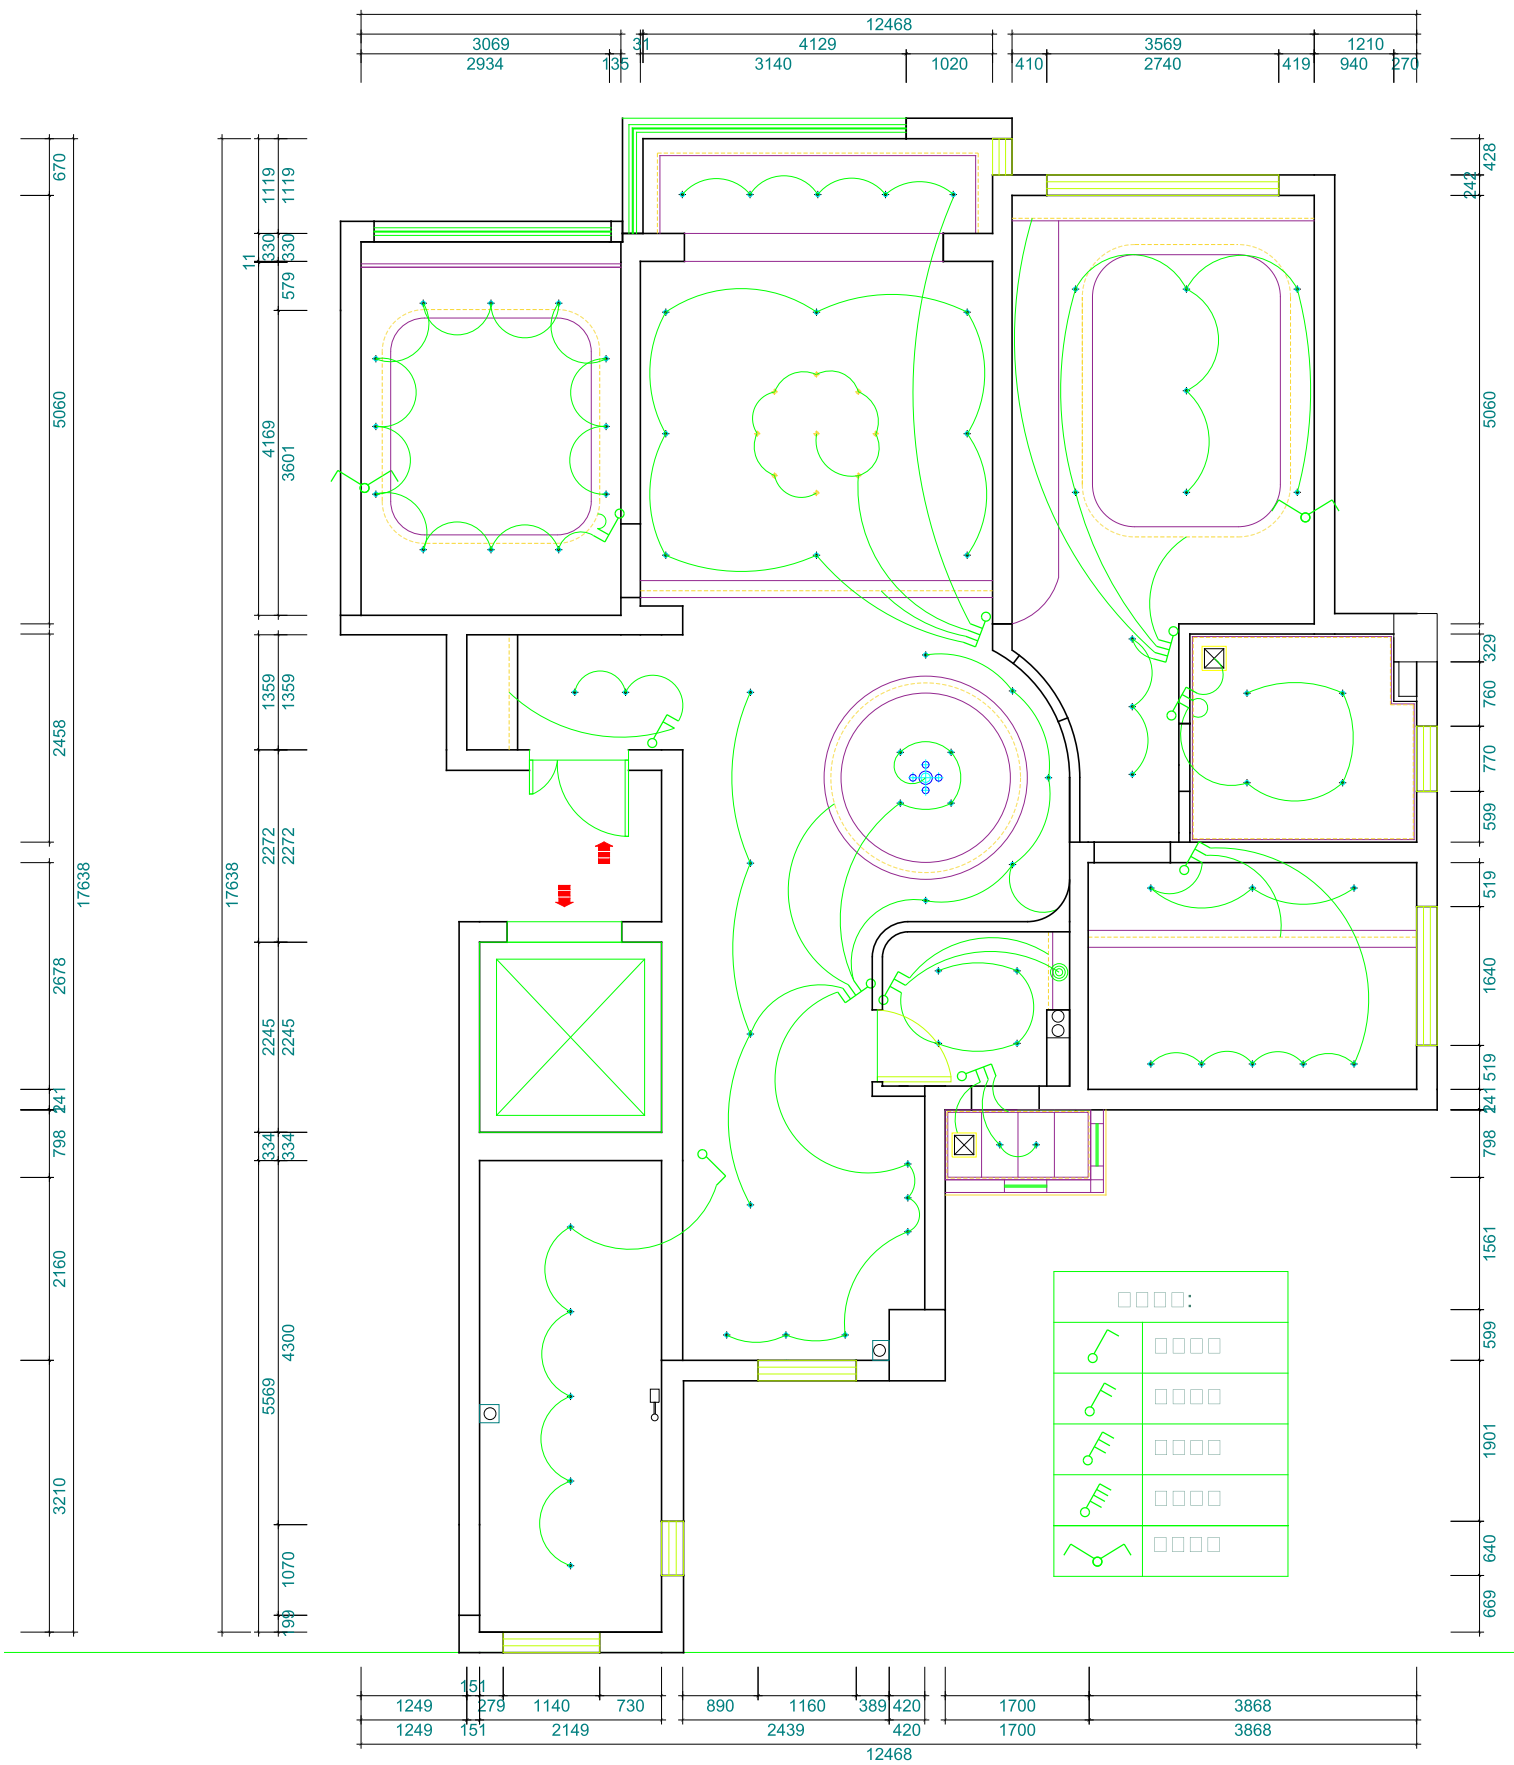


开关图

670
5060
2458
17638
2678
798
241
2160
3210

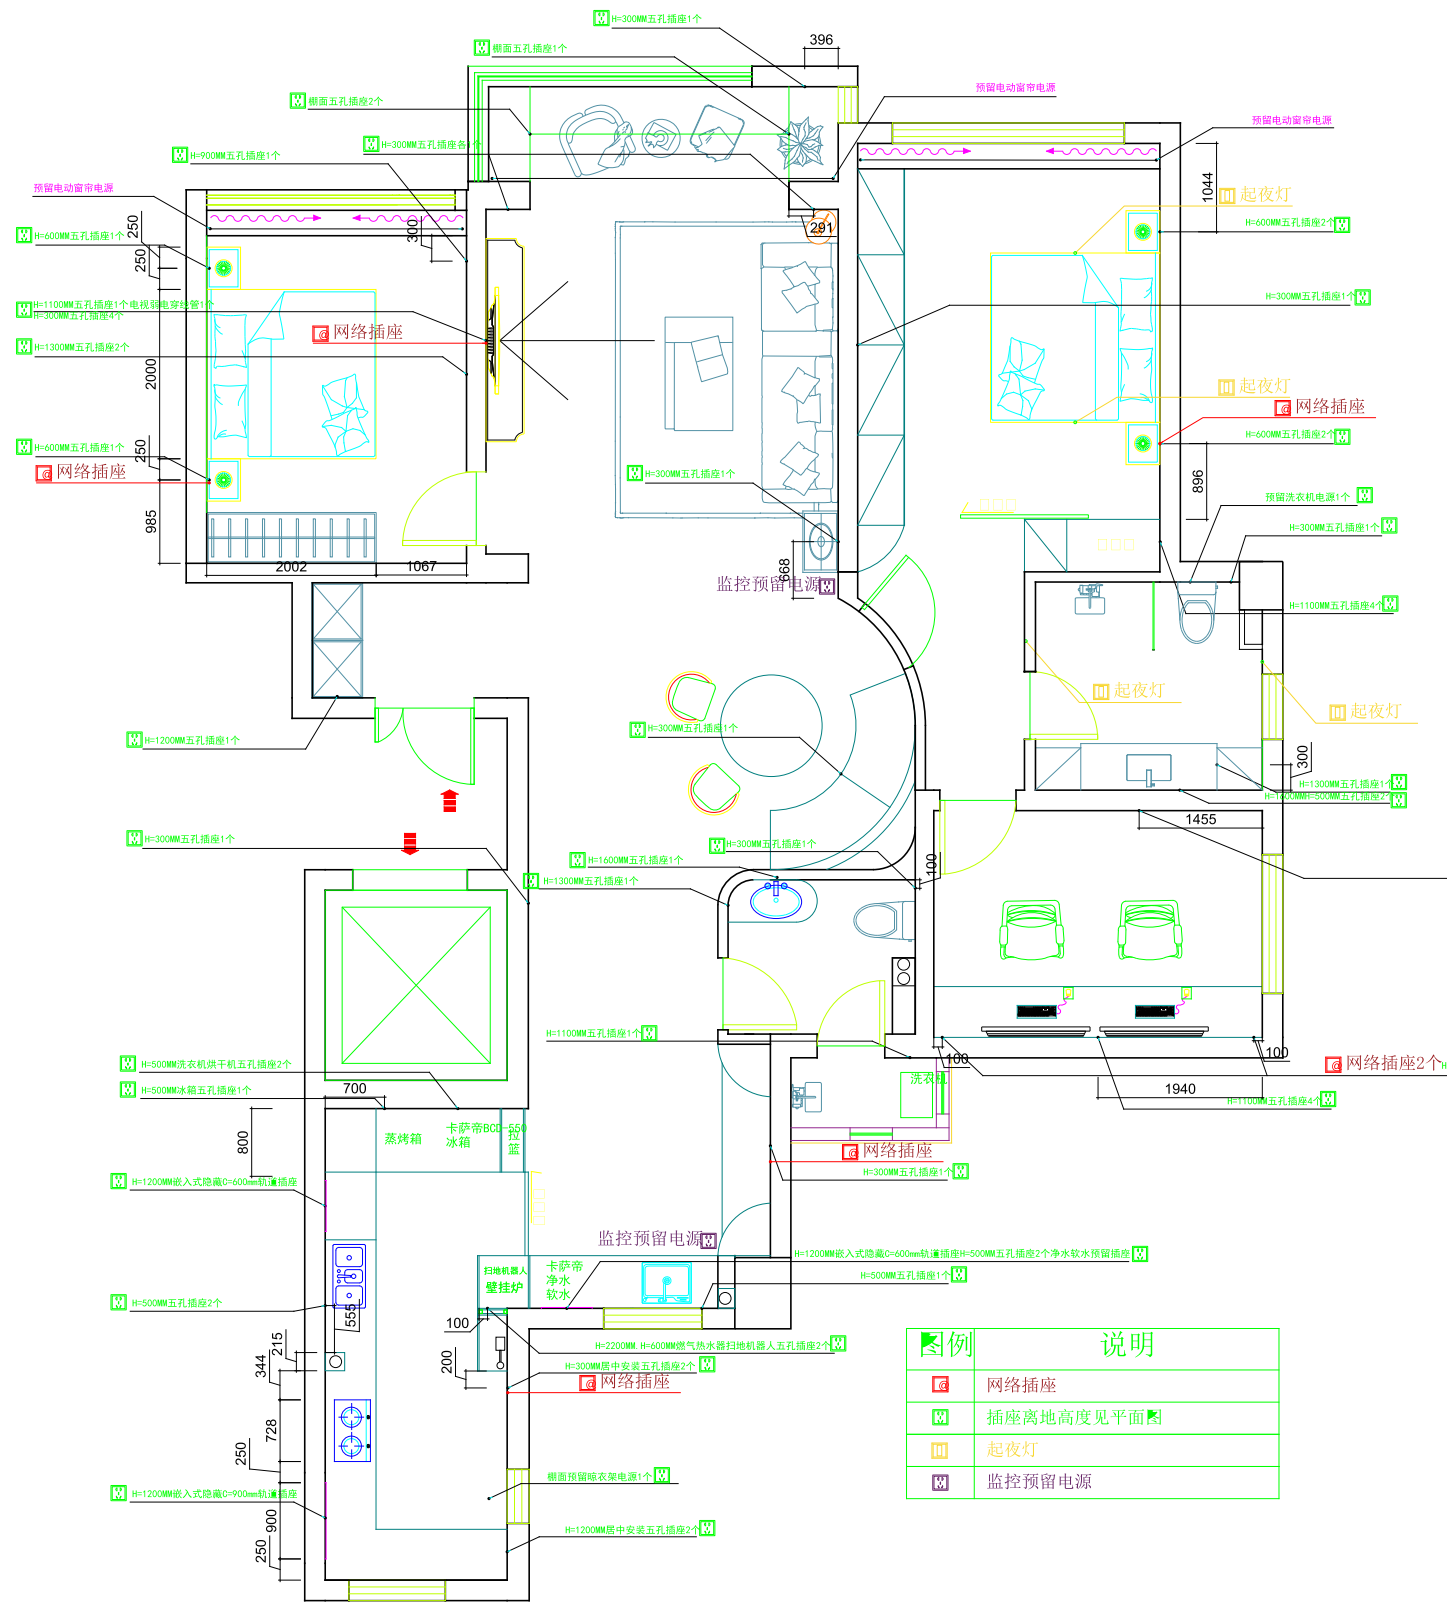

图例	说明
	网络插座
	插座离地高度见平面图
	起夜灯
	监控预留电源

插座位置图

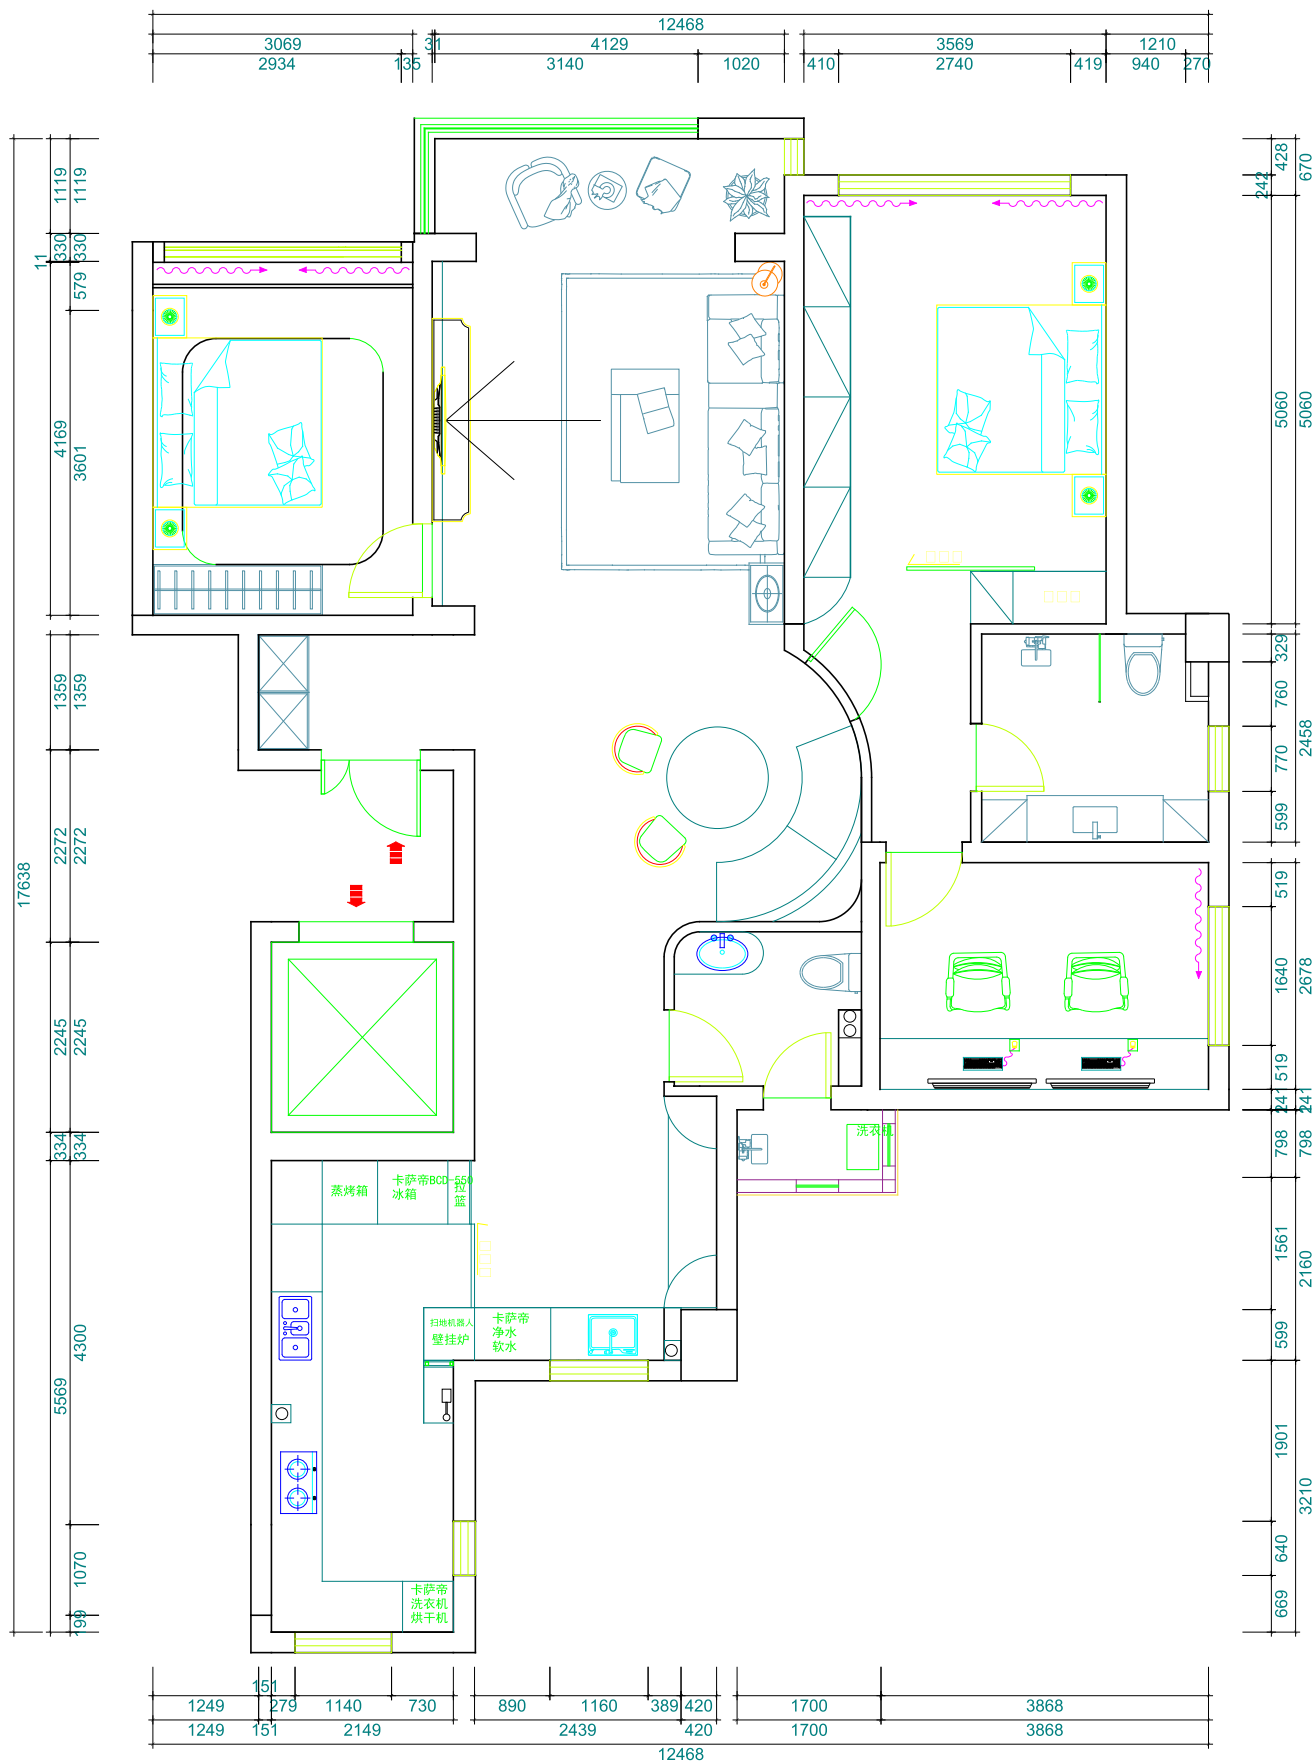

平面布置图